




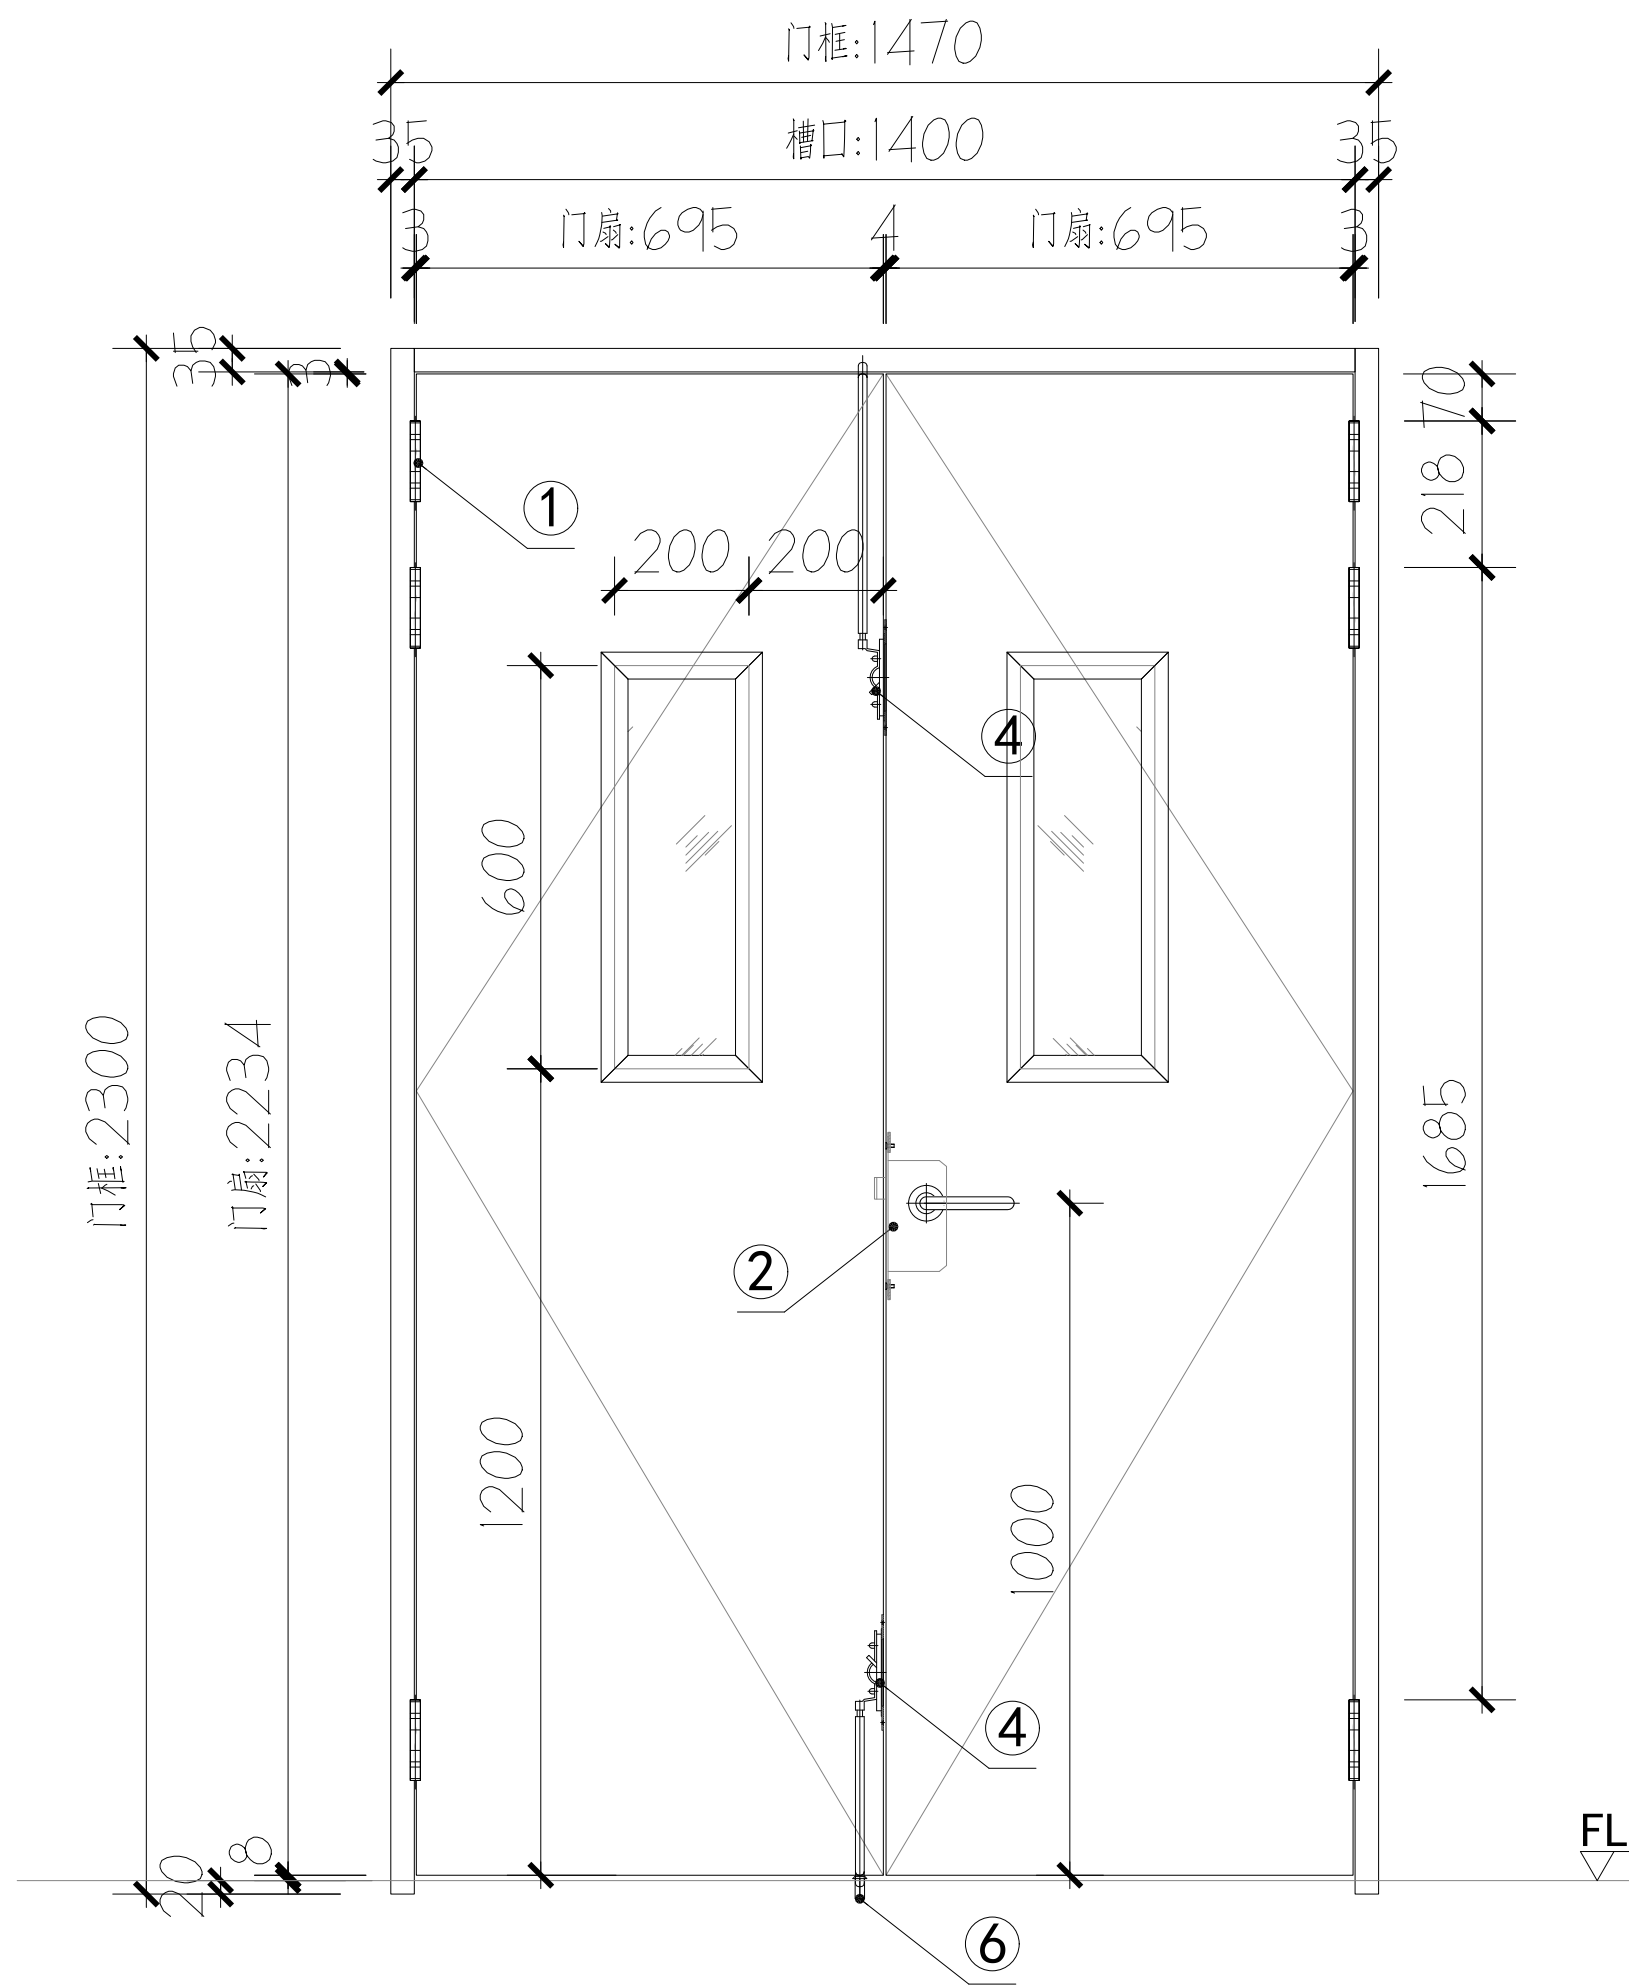


01 门体立面图（拉侧） 1:20

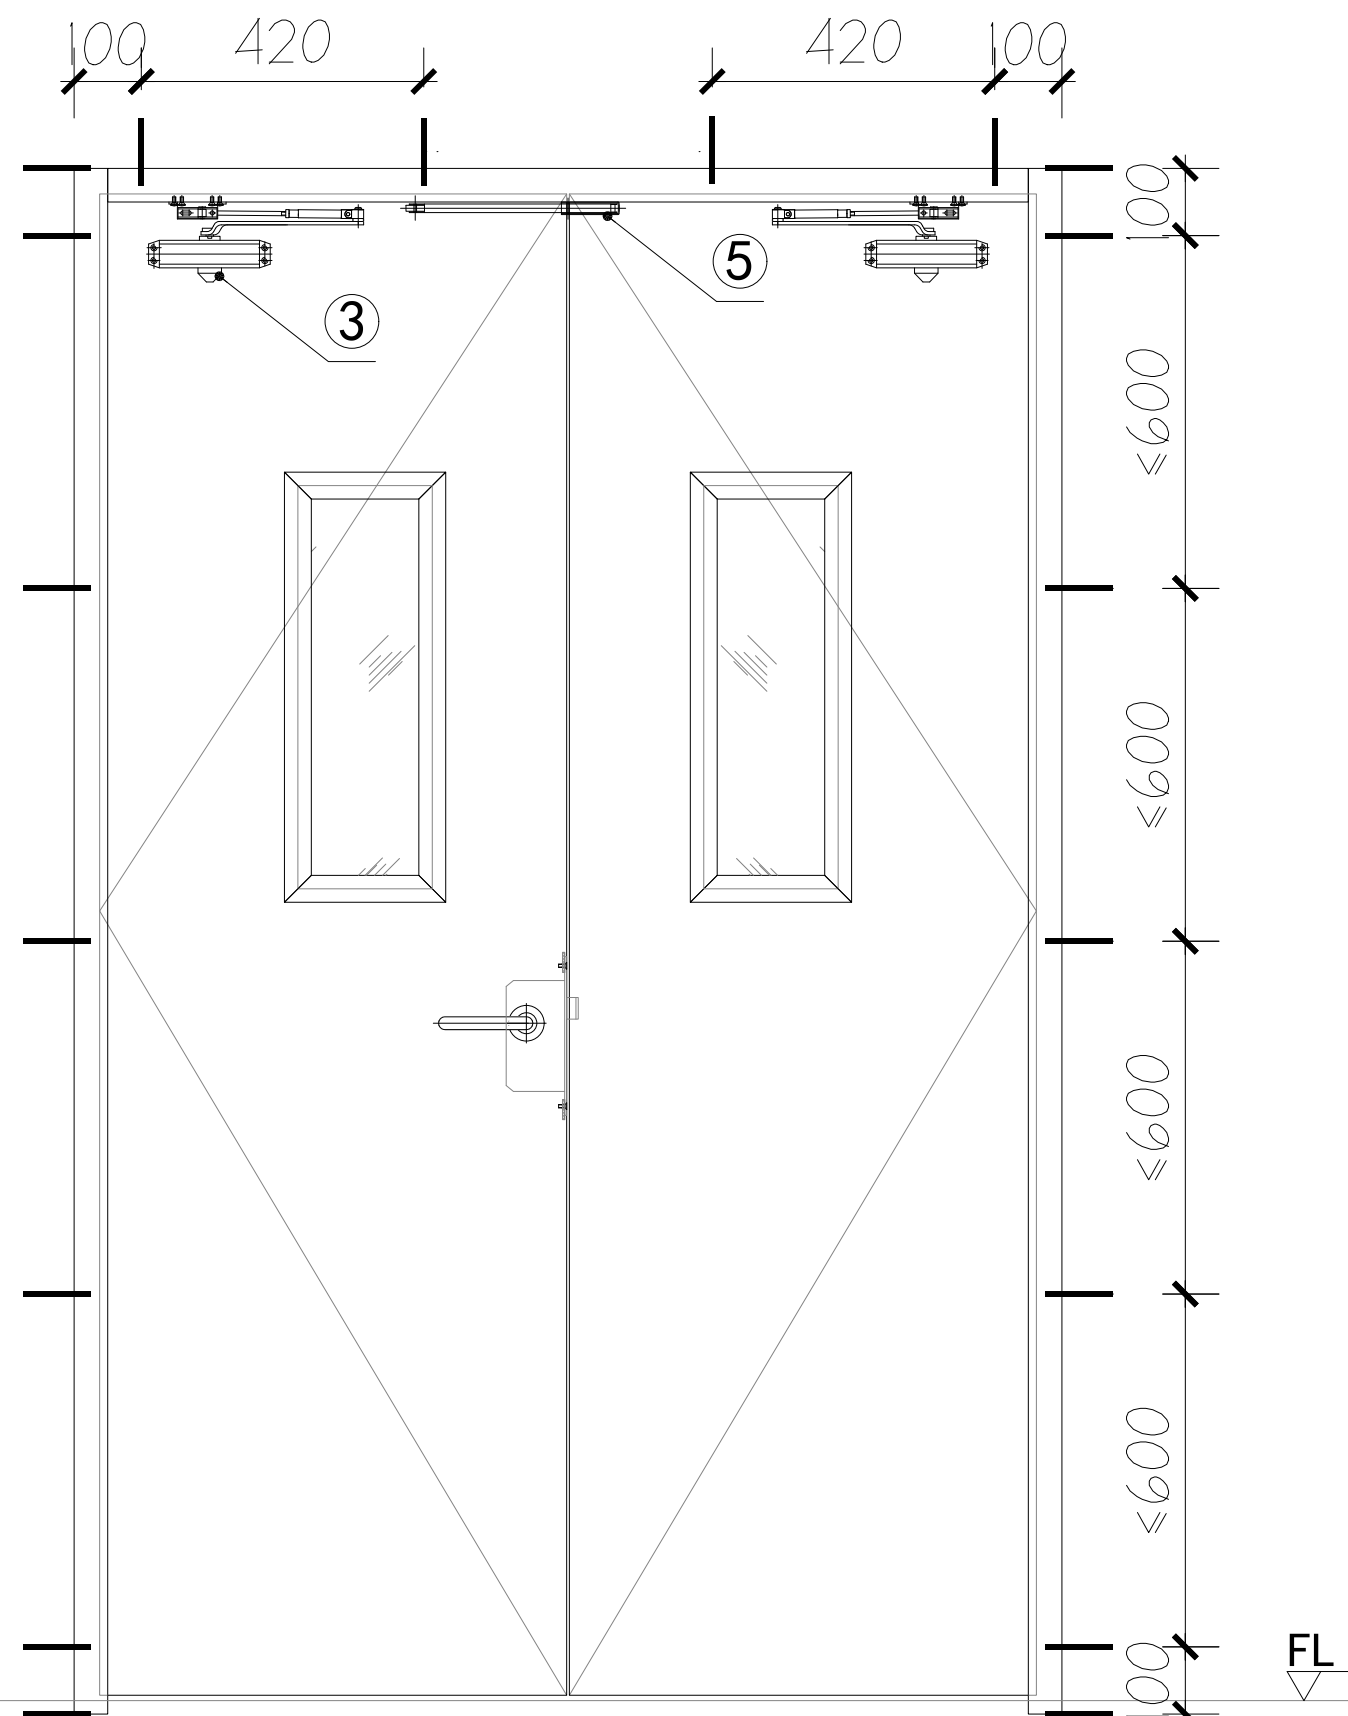

02 门体立面图（推侧） 1:20

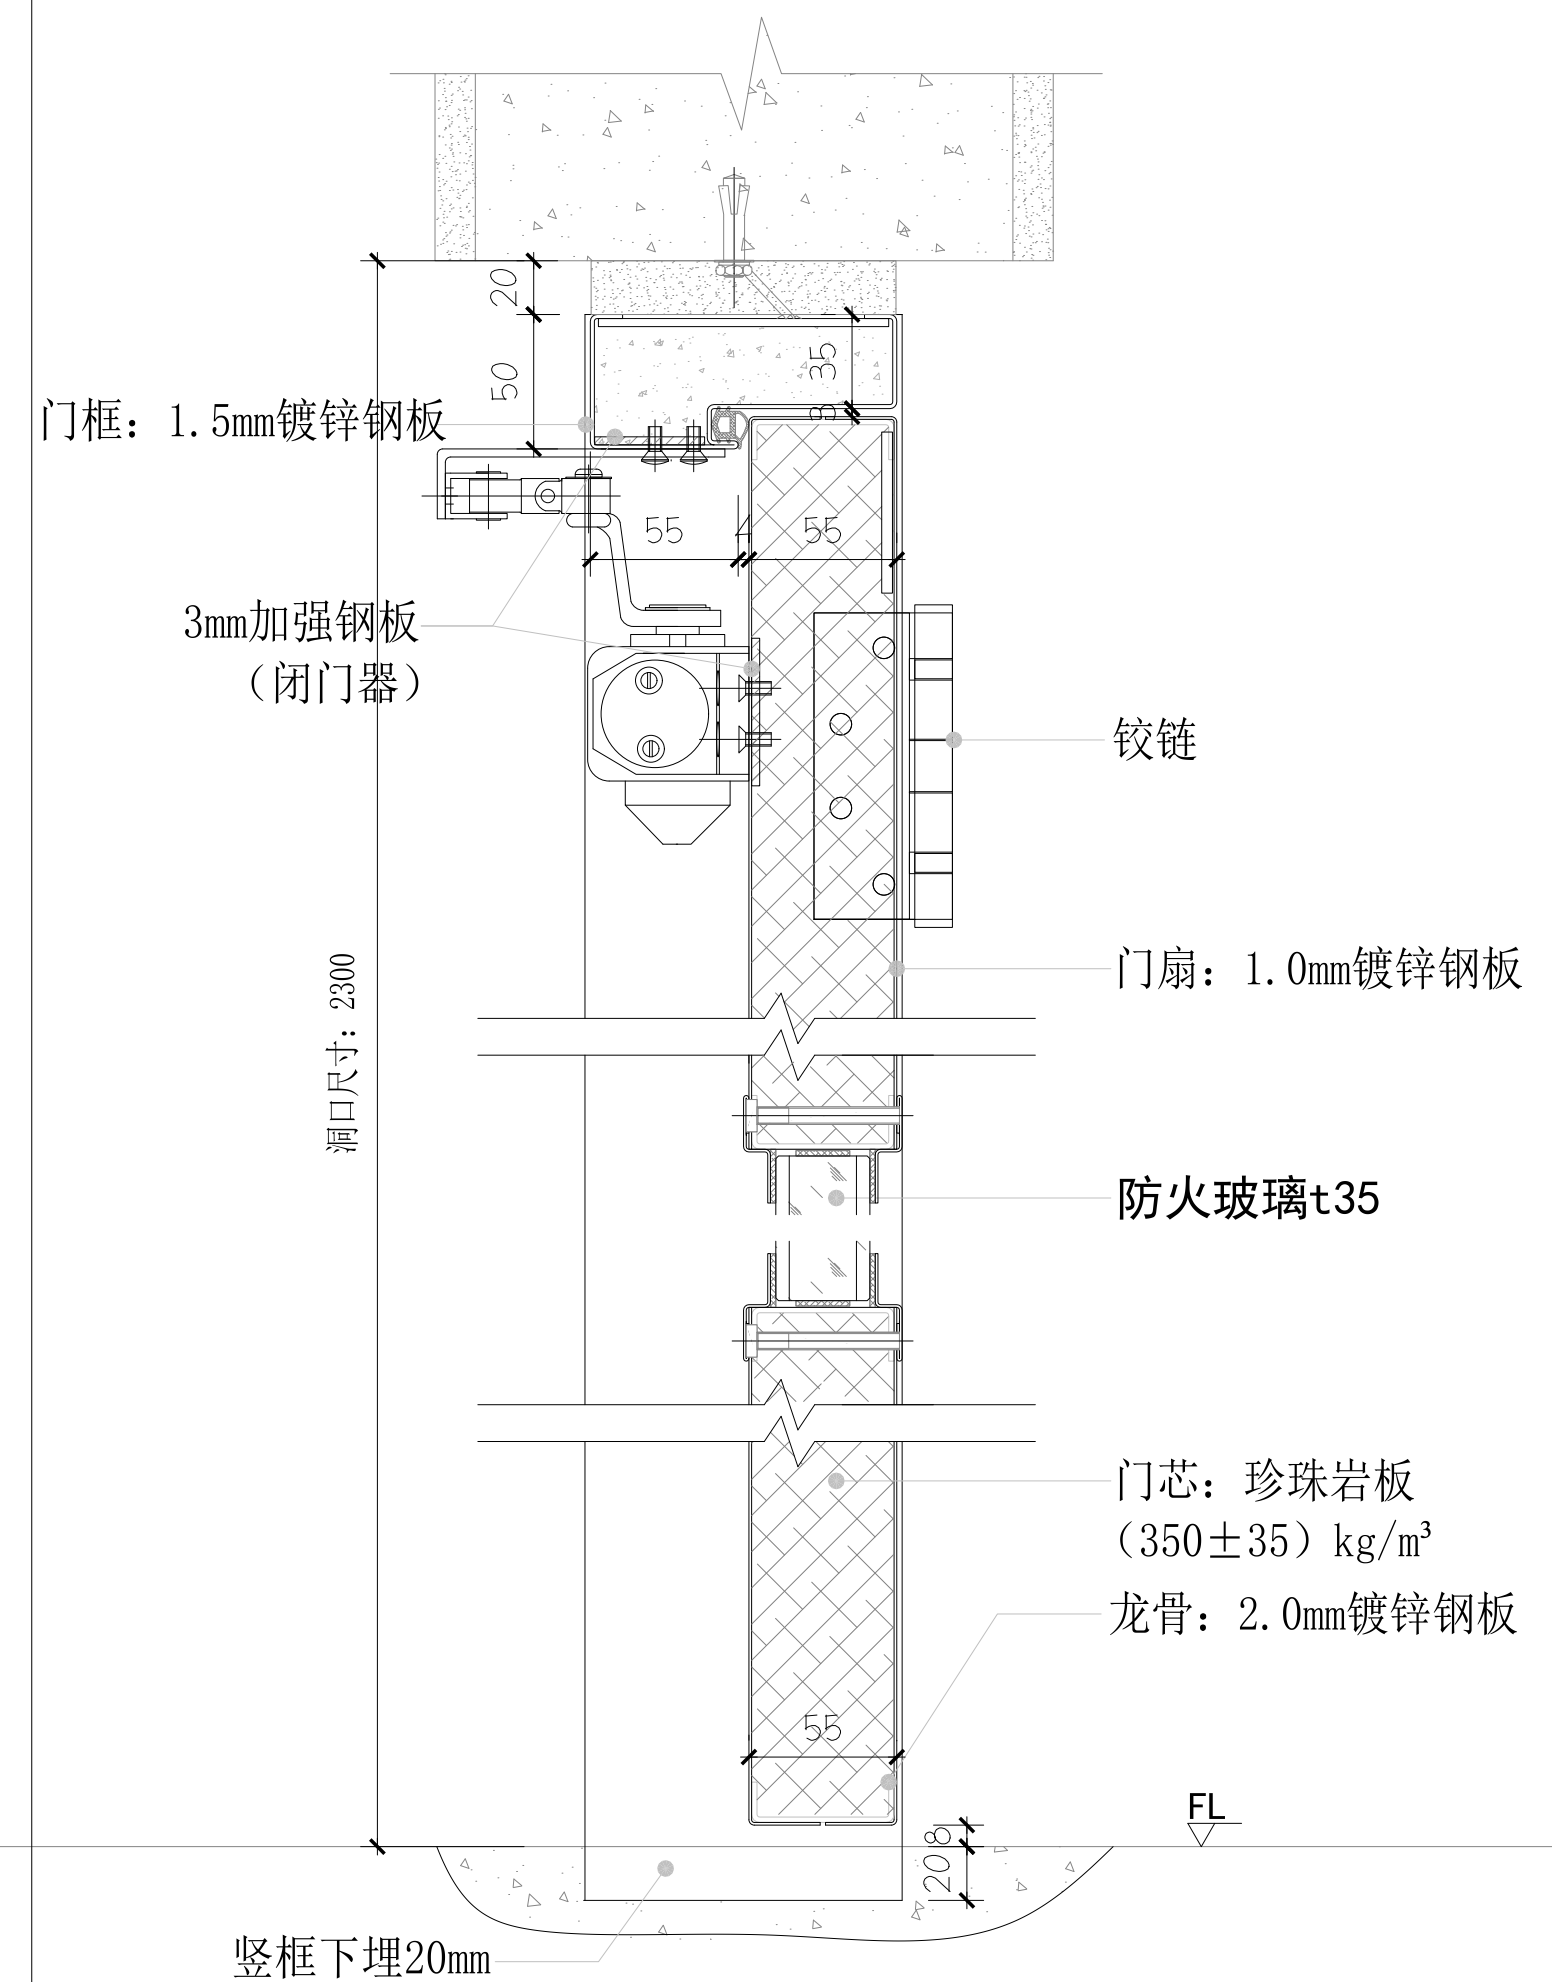

03 门体竖剖图 1:5

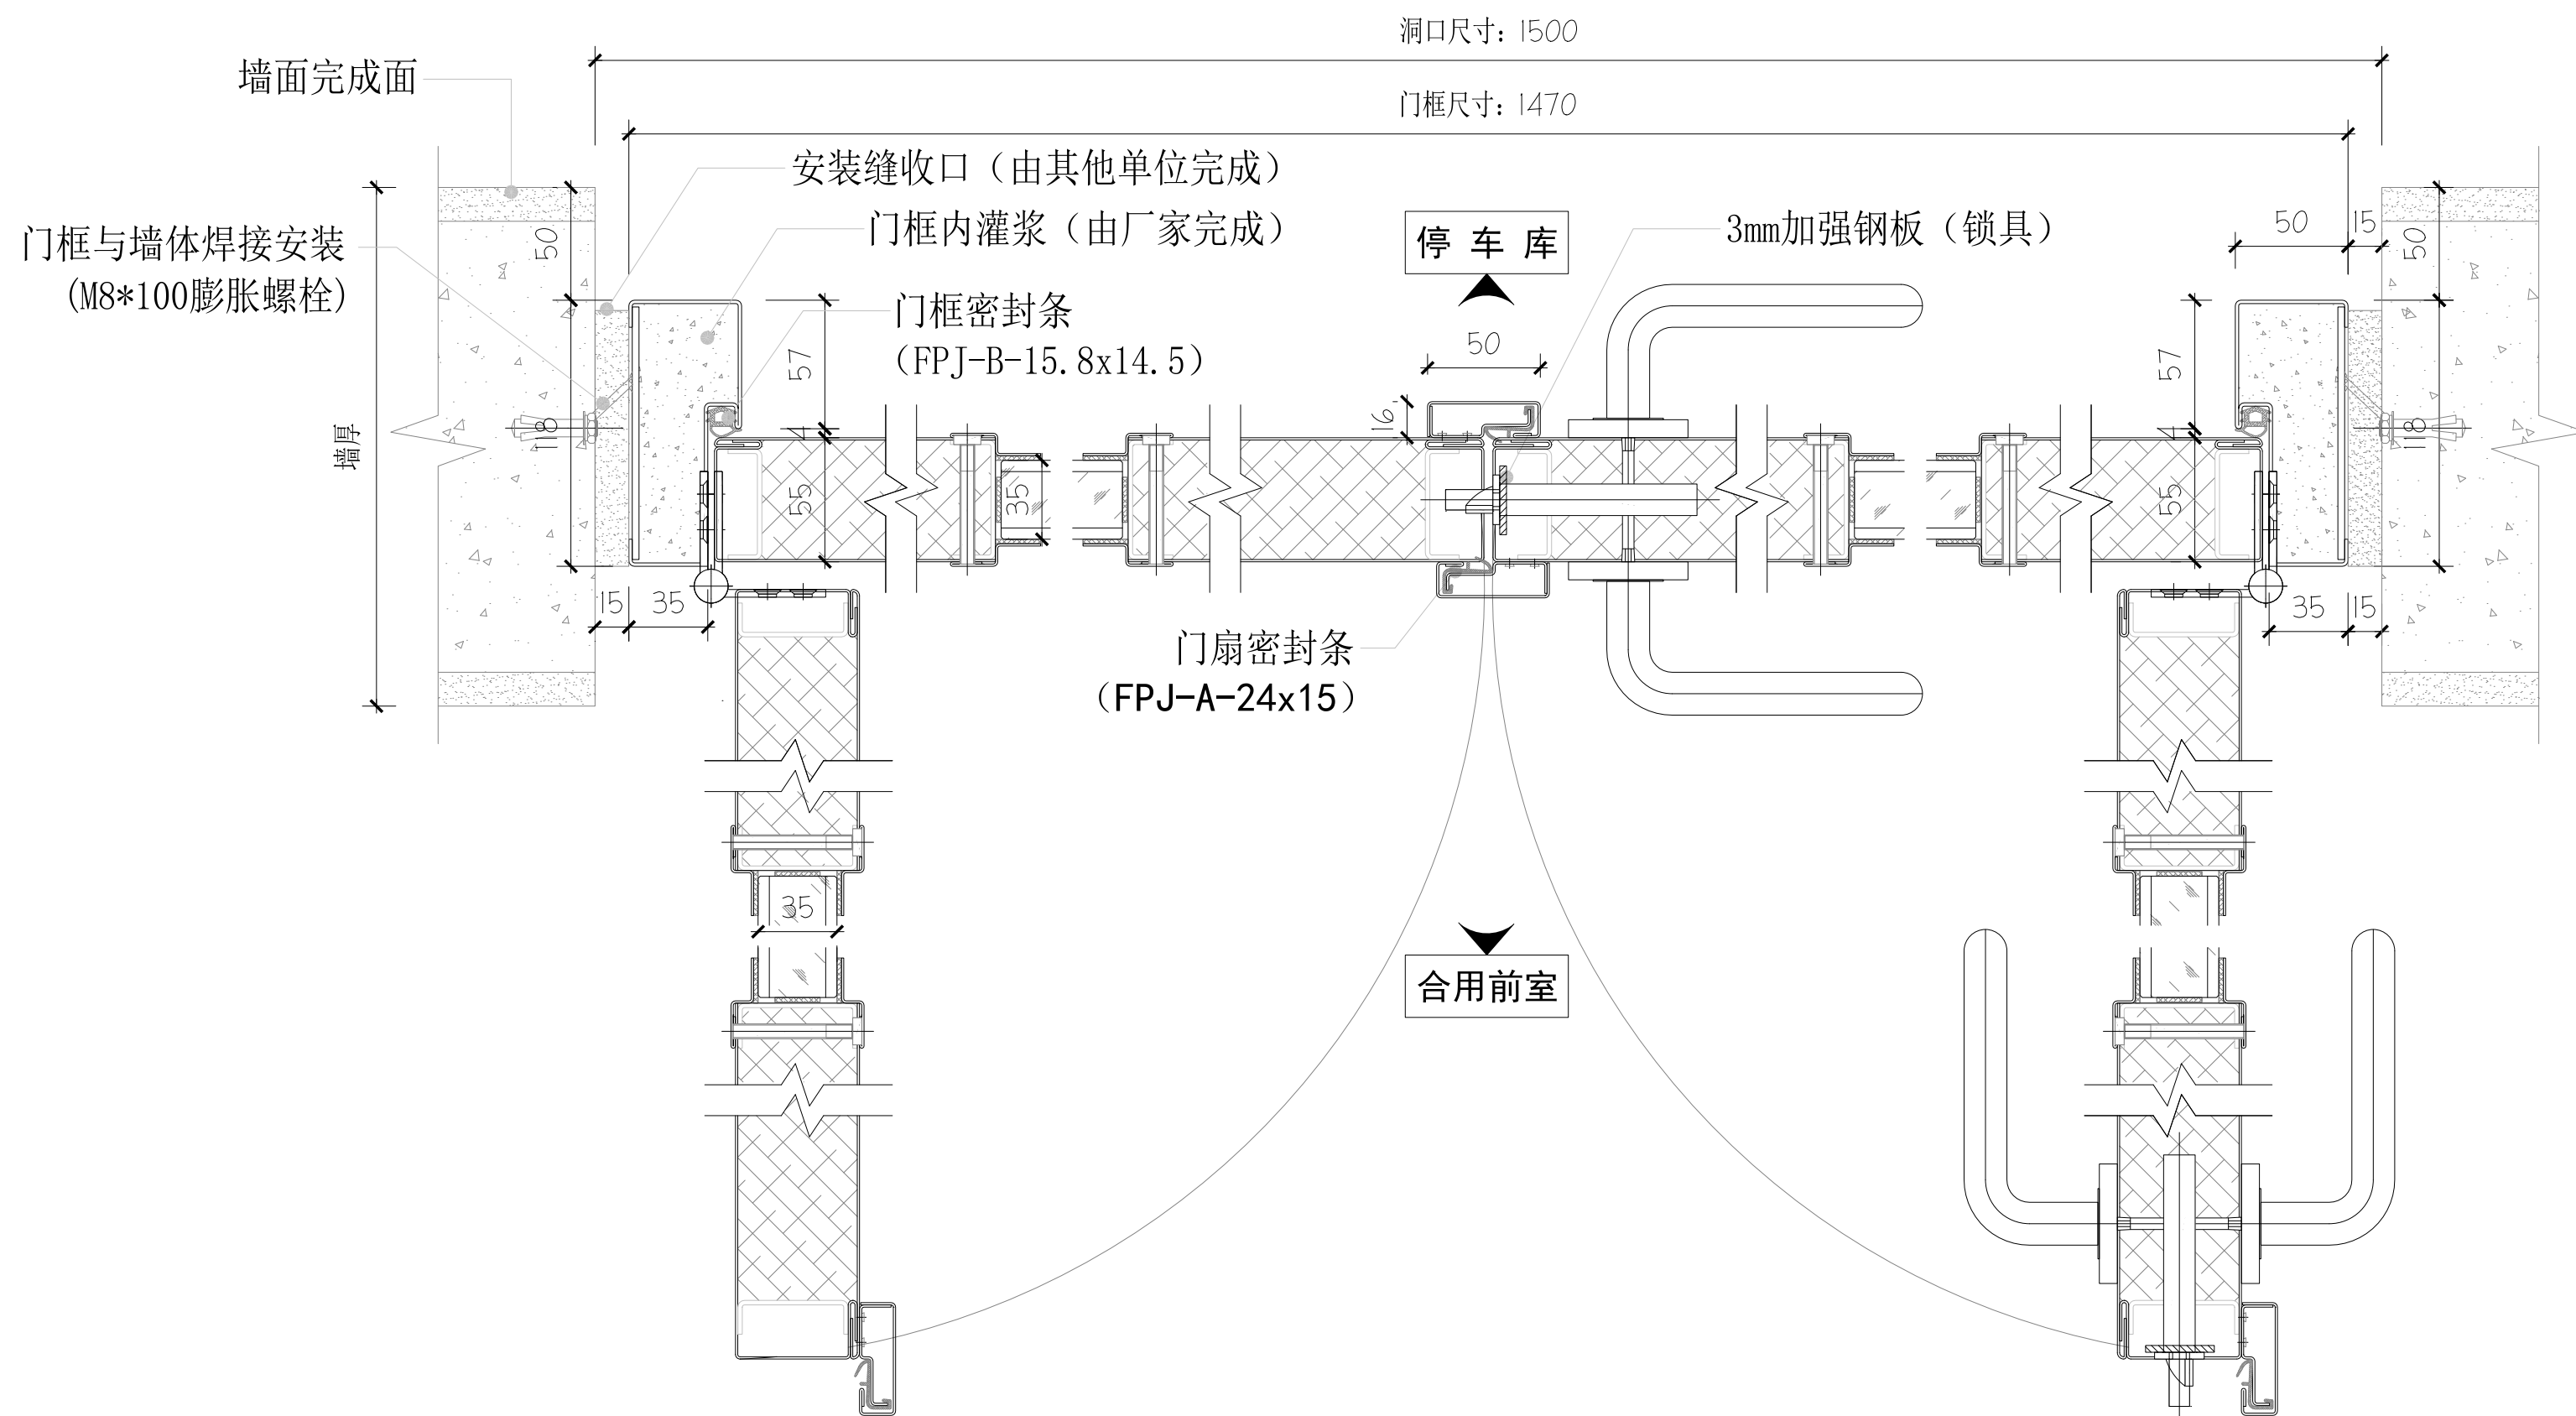

04 门体横剖图 1:5

钢质双扇隔热防火门(甲级)				
门 型		MGF (A) D1523. t		
门 编 号		10#		
洞口尺寸		1500*2300		
构件尺寸		1470*2300		
门框材质		镀锌钢板t1.5		
门扇材质		镀锌钢板t1.0		
门槛材质				
防火门芯		珍珠岩板（350±35）kg/m ³		
玻 璃		防火玻璃t35		
门框密封条		FPJ-B-15.8x14.5		
门扇密封条		FPJ-A-24x15		
五金配置				
名称		品牌	型号	数量
① 欧标轴承合页		Allegion	4.5x4x3	6
② 欧标通道锁		Allegion	EL3040+HT111	1
③ 欧标明装闭门器		Allegion	BT 121	2
④ 手动暗插销		Allegion	FB458 12"	2
⑤ L型顺位器		Allegion	L-DC	1
⑥ 防尘筒		Allegion	DP01	1
⑦				
饰面颜色		拉门侧：灰色粉末喷涂 推门侧：灰色粉末喷涂		

总承包单位		北京建工集团有限责任公司	
深化图			
项目总工：张志强		专业负责人：刁佳	
审核人：程宝发		绘图人：刁佳	
阶段：深化图		日期：2026/03/31	
版次		发布日期	
A		2024/09/22	
0		2025/06/24	
0A		2026/03/31	
项目： 其他类多功能用地项目（1#办公楼等4项） 北京城市副中心1202街区FZX-1202-0001地块F3			
图纸名称：		10#门深化图	
图号：		SLDS-BCEG-000-SDS-DW-FHM129	
图幅：		A1	